

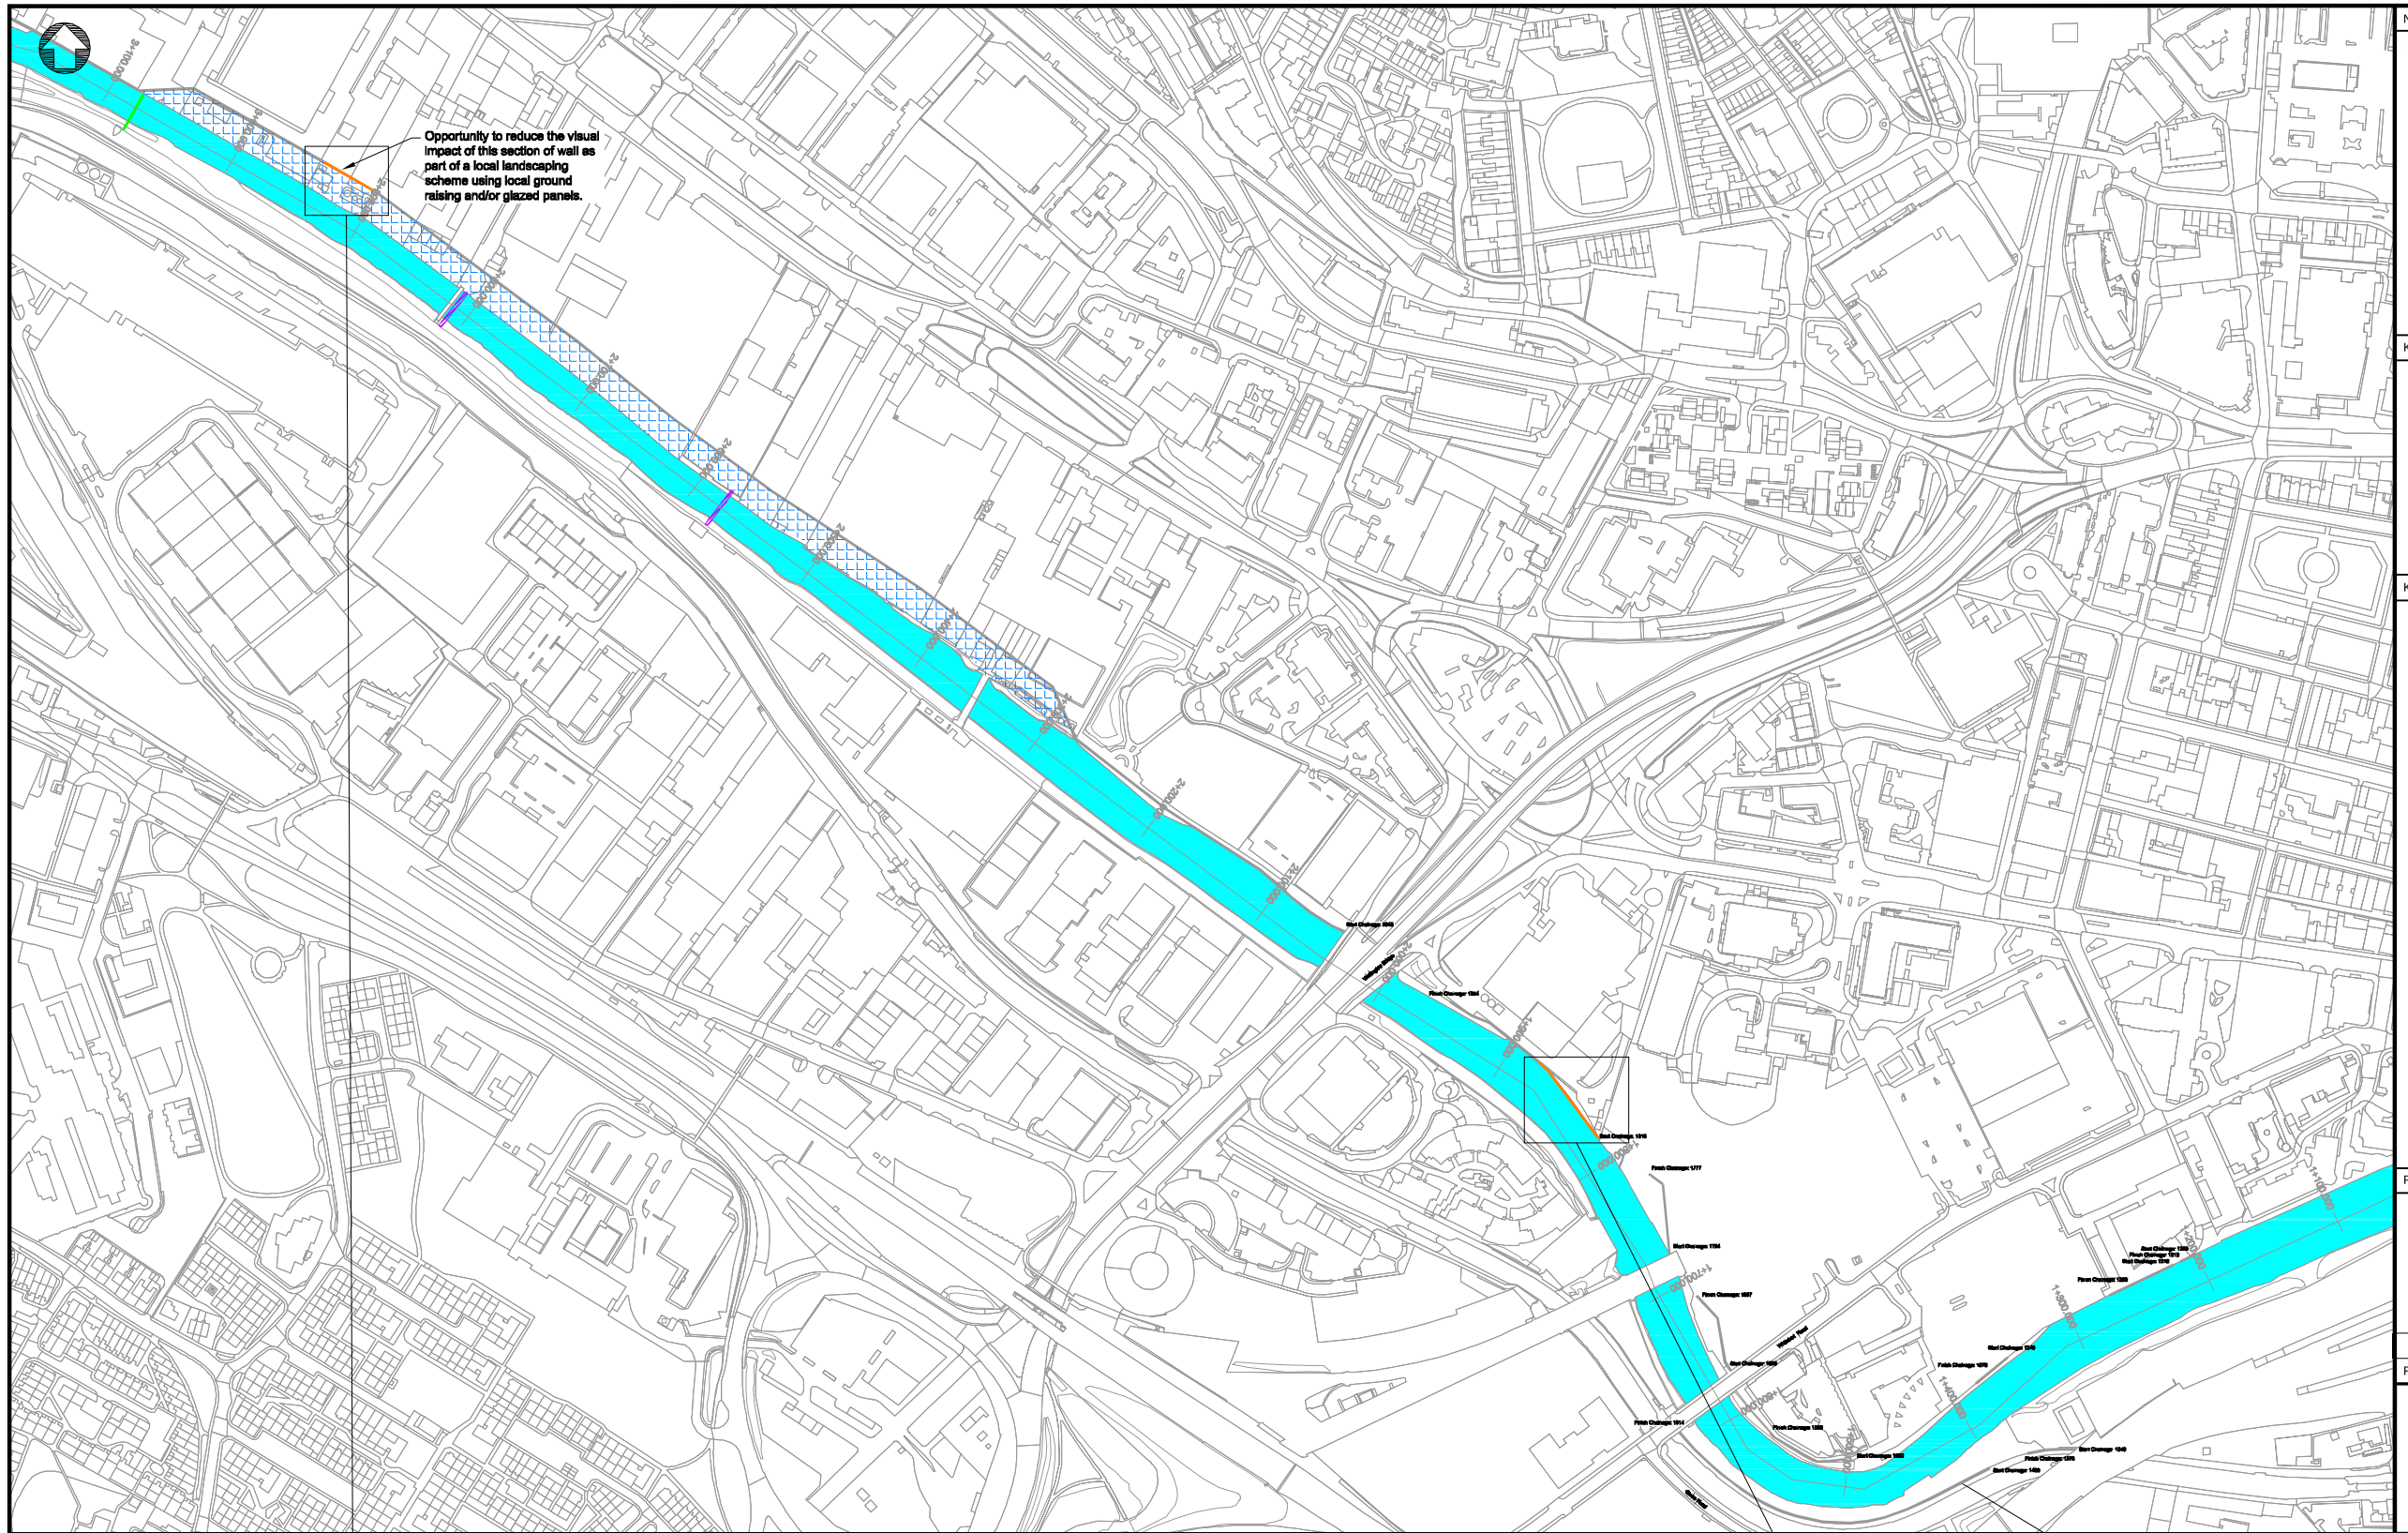


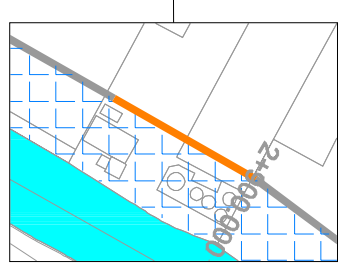

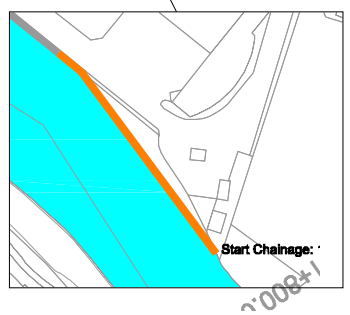

Part Plan on Scheme
Sheet 1 of 4
Scale 1:2500

© Mott MacDonald 2014

This document is issued for the party which commissioned it and for specific purposes connected with the captioned project only. It should not be relied upon by any other party or used for any other purpose. We accept no responsibility for the consequences of this document being relied upon by any other party, or being used for any other purpose, or containing any error or omission which is due to an error or omission in data supplied to us by other parties.

P:\Sheffield\372991 - Leeds FAS2 PJC\5.0 MM Drawings\CAD\Working drawings\Civil\Drawings\Leeds No Rodley 1100 - 1103.dwg Dec 4, 2017 - 4:54PM mar09252

Notes

1. All levels are in metres above Ordnance Datum unless noted otherwise.
2. All dimensions are in millimetres unless noted otherwise.
3. Access and working space to be agreed with landowner and tenants.
4. Wall heights are based on a Standard of Protection of 200 year with climate change to 2069 (including NFM) with construction of attenuation at Calverley only.

Key to symbols

- Height less than 1.5m
- Defence Location - Height between 1.5 - 1.8m
- Defence Location - Height greater 1.8m
- Pipe Obstruction
- Bridge Obstruction
- Attenuation Zone

Key Plan

DRAFT

1:2500 0 125m 250m

RESIDUAL RISK ASSESSMENT

Wherever possible, risk is designed-out of this proposal during the design process. Where this is not possible, the risk will be minimised and any residual significant risk will be noted and indicated by the symbol.

Reference drawings

Rev	Date	Drawn	Description	Ch'k'd	App'd
P1	29/11/17	AM	For Comment	PJC	CSG

bmmjv
bam nuttall · M MOTT MACDONALD
Environment Agency · Arup · thomas mackay

4th Floor, Derwent House
150 Arundel Gate
Sheffield, S1 2JY
United Kingdom
T +44 (0)114 2761242
F
w www.mottmac.com

Leeds CITY COUNCIL


Title
Leeds Flood Alleviation Scheme

Indicative Scheme Details
Sheet 1 of 4

Designed	F Buskevicius	FB	Eng check	P J Charlesworth	PJC
Drawn	A Marsden	AM	Coordination	P J Charlesworth	PJC
Dwg check	F Buskevicius	FB	Approved	C S Greensill	CSG

Scale at A1	Status	Rev
As Shown	PRE	P1

Drawing Number
LFD-BMM-ZX-XX-DR-CC-01100

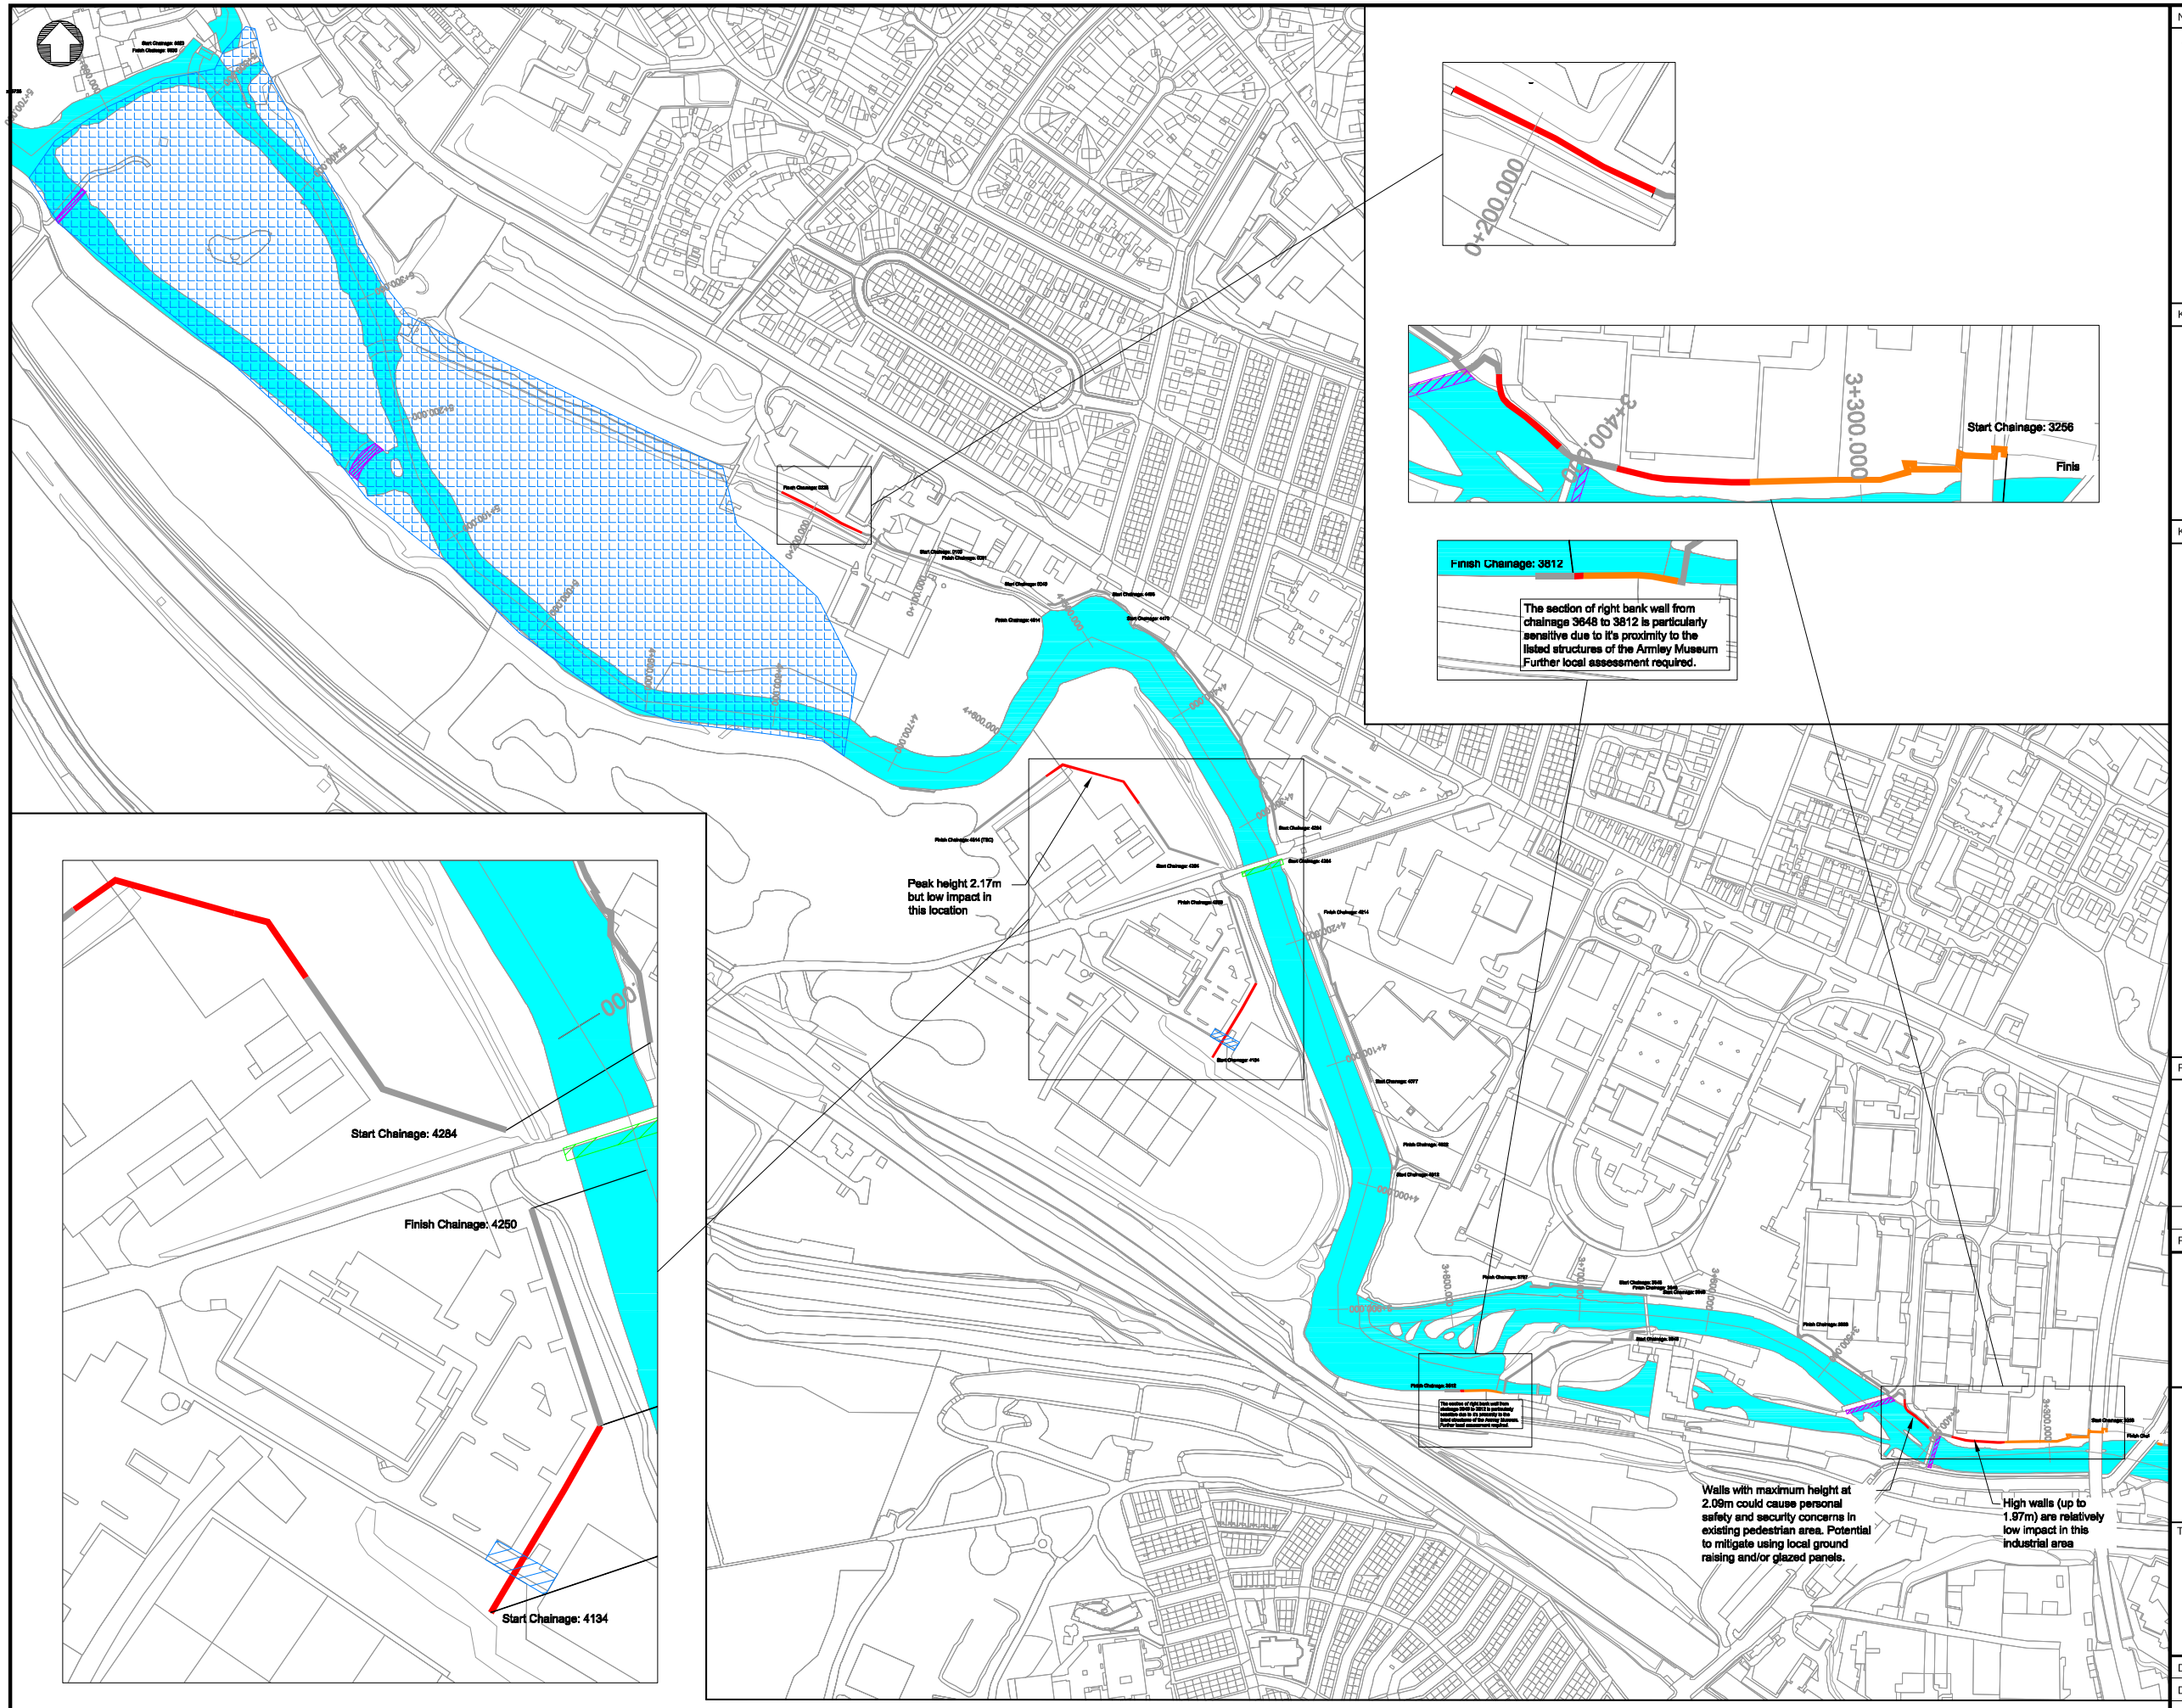

Part Plan on Scheme
Sheet 2 of 4
Scale 1:2500

Notes

1. All levels are in metres above Ordnance Datum unless noted otherwise.
2. All dimensions are in millimetres unless noted otherwise.
3. Access and working space to be agreed with landowner and tenants.
4. Wall heights are based on a Standard of Protection of 200 year with climate change to 2069 (including NFM) with construction of attenuation at Calverley only.

Key to symbols

- Height less than 1.5m
- Defence Location - Height between 1.5 - 1.8m
- Defence Location - Height greater 1.8m
- Pipe Obstruction
- Bridge Obstruction
- Attenuation Zone

Key Plan

DRAFT

1:2500 0 125m 250m

RESIDUAL RISK ASSESSMENT
Wherever possible, risk is designed-out of this proposal during the design process. Where this is not possible, the risk will be minimised and any residual significant risk will be noted and indicated by the symbol.

Reference drawings

Rev	Date	Drawn	Description	Ch'k'd	App'd
P1	29/11/17	AM	For Comment	PJC	CSG

bmmjv
bam nuttall | M MOTT MACDONALD
Environment Agency | Arup | thomas mackay
4th Floor, Derwent House
150 Arundel Gate
Sheffield, S1 2JY
United Kingdom
T +44 (0)114 2761242
F
W www.mottmac.com

Leeds CITY COUNCIL

Title
Leeds Flood Alleviation Scheme

Indicative Scheme Details
Sheet 2 of 4

Designed	F Buskevicius	FB	Eng check	P J Charlesworth	PJC
Drawn	A Marsden	AM	Coordination	P J Charlesworth	PJC
Dwg check	F Buskevicius	FB	Approved	C S Greensill	CSG

Scale at A1	Status	Rev
As Shown	PRE	P1

Drawing Number
LFD-BMM-ZX-XX-DR-CC-01101


© Mott MacDonald 2014


This document is issued for the party which commissioned it and for specific purposes connected with the captioned project only. It should not be relied upon by any other party or used for any other purpose. We accept no responsibility for the consequences of this document being relied upon by any other party, or being used for any other purpose, or containing any error or omission which is due to an error or omission in data supplied to us by other parties.


Limited impact of wall (up to 1.7m) due to proximity to railway and potential to reduce with local raising.


Potential for all defences along this length to be formed as an earth embankment or for local ground levels altered and tree planting to reduce visual impact of defence.


Peak height 2.17m but low impact in this location

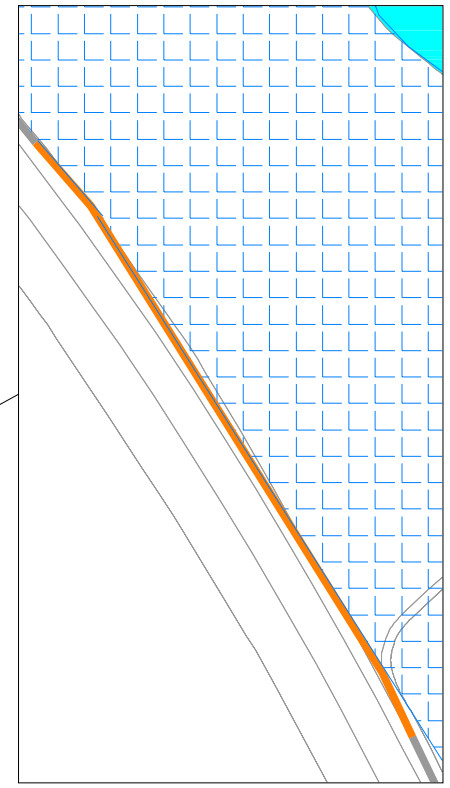

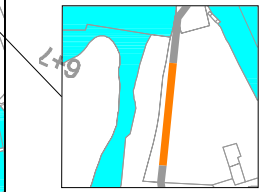

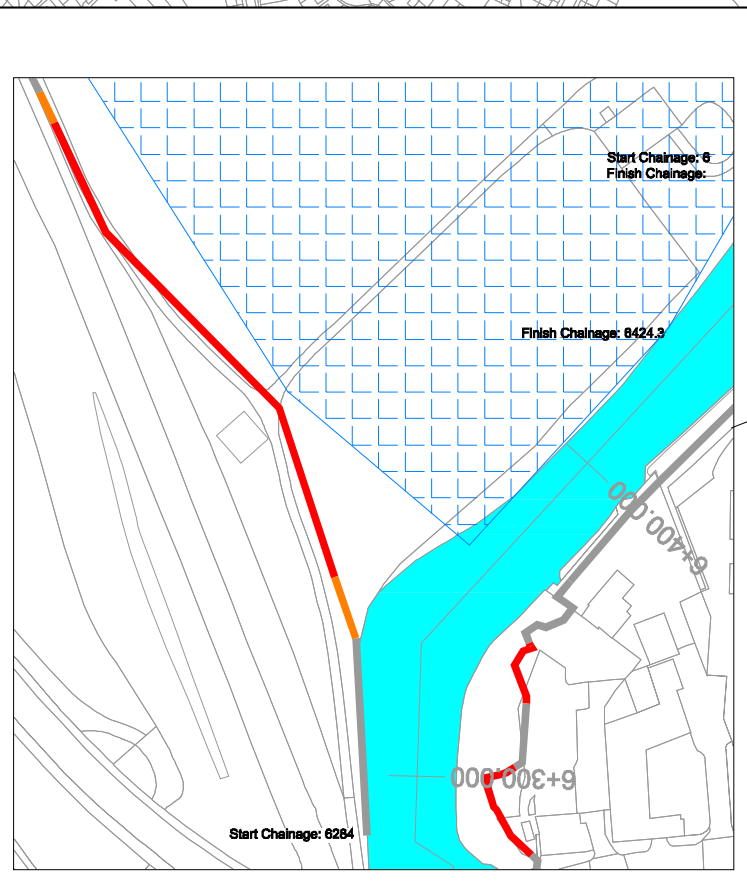

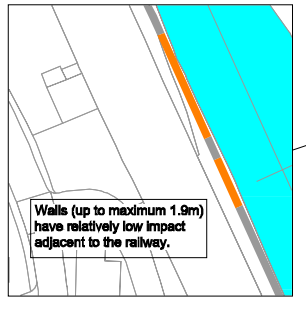

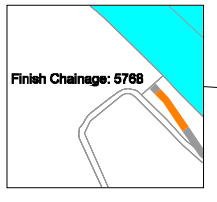

Kirkstall Bridge Inn - Very high defences required if placed near river. Potential to reduce the impact by defending the building and allowing the terrace to flood, but floodgates that require closing during an event would be needed. Potential for glazed panels to be incorporated into walls.

Part Plan on Scheme
Sheet 3 of 4
Scale 1:2500

Notes

1. All levels are in metres above Ordnance Datum unless noted otherwise.
2. All dimensions are in millimetres unless noted otherwise.
3. Access and working space to be agreed with landowner and tenants.
4. Wall heights are based on a Standard of Protection of 200 year with climate change to 2069 (including NFM) with construction of attenuation at Calverley only.

Key to symbols

- Height less than 1.5m
- Defence Location - Height between 1.5 - 1.8m
- Defence Location - Height greater 1.8m
- Pipe Obstruction
- Bridge Obstruction
- Attenuation Zone

Key Plan

DRAFT

1:2500 0 125m 250m

RESIDUAL RISK ASSESSMENT
Wherever possible, risk is designed-out of this proposal during the design process. Where this is not possible, the risk will be minimised and any residual significant risk will be noted and indicated by the symbol.

Reference drawings

Rev	Date	Drawn	Description	Ch'k'd	App'd
P1	29/11/17	AM	For Comment	PJC	CSG

bmmjv
bam Nuttall · M · M
Environment Agency · Arup · thomas | mackay
4th Floor, Derwent House
150 Arundel Gate
Sheffield, S1 2JY
United Kingdom
T +44 (0)114 2761242
F
W www.mottmac.com

Leeds City Council

Title
Leeds Flood Alleviation Scheme

Indicative Scheme Details
Sheet 3 of 4

Designed	F Buskevicius	FB	Eng check	P J Charlesworth	PJC
Drawn	A Marsden	AM	Coordination	P J Charlesworth	PJC
Dwg check	F Buskevicius	FB	Approved	C S Greensill	CSG


Scale at A1	Status	Rev
As Shown	PRE	P1


Drawing Number
LFD-BMM-ZX-XX-DR-CC-01102

© Mott MacDonald 2014

This document is issued for the party which commissioned it and for specific purposes connected with the captioned project only. It should not be relied upon by any other party or used for any other purpose. We accept no responsibility for the consequences of this document being relied upon by any other party, or being used for any other purpose, or containing any error or omission which is due to an error or omission in data supplied to us by other parties.

Limited impact of wall (up to 1.7m) due to proximity to railway and potential to reduce with local raising.

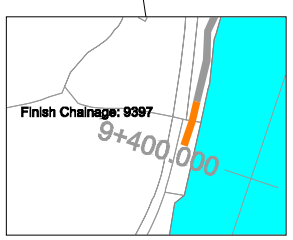

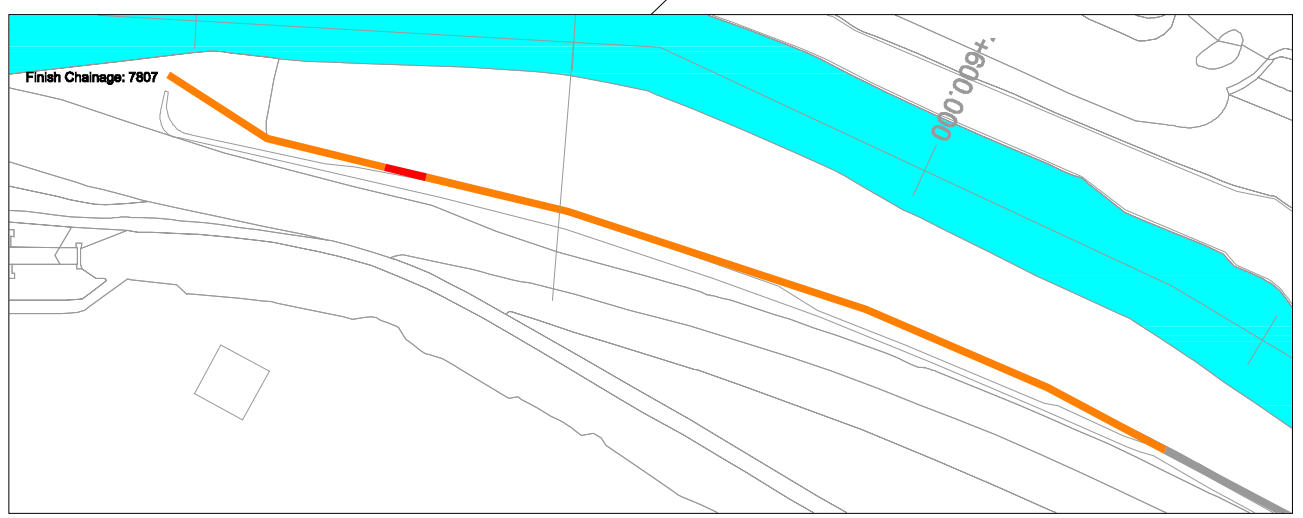

Part Plan on Scheme
Sheet 4 of 4

Scale 1:2500

© Mott MacDonald 2014

This document is issued for the party which commissioned it and for specific purposes connected with the captioned project only. It should not be relied upon by any other party or used for any other purpose. We accept no responsibility for the consequences of this document being relied upon by any other party, or being used for any other purpose, or containing any error or omission which is due to an error or omission in data supplied to us by other parties.

P:\Sheffield\372991 - Leeds FAS2 PJC\5.0 MM Drawings\CAD\Working drawings\Civil\Drawings\Leeds No Rodley 1100 - 1103.dwg Dec 4, 2017 - 4:49PM mar09252

Notes

1. All levels are in metres above Ordnance Datum unless noted otherwise.
2. All dimensions are in millimetres unless noted otherwise.
3. Access and working space to be agreed with landowner and tenants.
4. Wall heights are based on a Standard of Protection of 200 year with climate change to 2069 (including NFM) with construction of attenuation at Calverley only.

Key to symbols

- Height less than 1.5m
- Defence Location - Height between 1.5 - 1.8m
- Defence Location - Height greater 1.8m
- Pipe Obstruction
- Bridge Obstruction
- Attenuation Zone

Key Plan

DRAFT

1:2500 0 125m 250m

RESIDUAL RISK ASSESSMENT

Wherever possible, risk is designed-out of this proposal during the design process. Where this is not possible, the risk will be minimised and any residual significant risk will be noted and indicated by the symbol.

Reference drawings

Rev	Date	Drawn	Description	Ch'k'd	App'd
P1	29/11/17	AM	For Comment	PJC	CSG

bmmjv
bam nuttall | M M
Environment Agency | Arup | thomas mackay
4th Floor, Derwent House
150 Arundel Gate
Sheffield, S1 2JY
United Kingdom
T +44 (0)114 2761242
F
W www.mottmac.com

Leeds City Council

Title

Leeds Flood Alleviation Scheme

Indicative Scheme Details
Sheet 4 of 4

Designed	F Buskevicius	FB	Eng check	P J Charlesworth	PJC
Drawn	A Marsden	AM	Coordination	P J Charlesworth	PJC
Dwg check	F Buskevicius	FB	Approved	C S Greensill	CSG

Scale at A1	Status	Rev
As Shown	PRE	P1

Drawing Number

LFD-BMM-ZX-XX-DR-CC-01103